


photo #2

Camion de raclage

decoking truck



DECOKE B-102

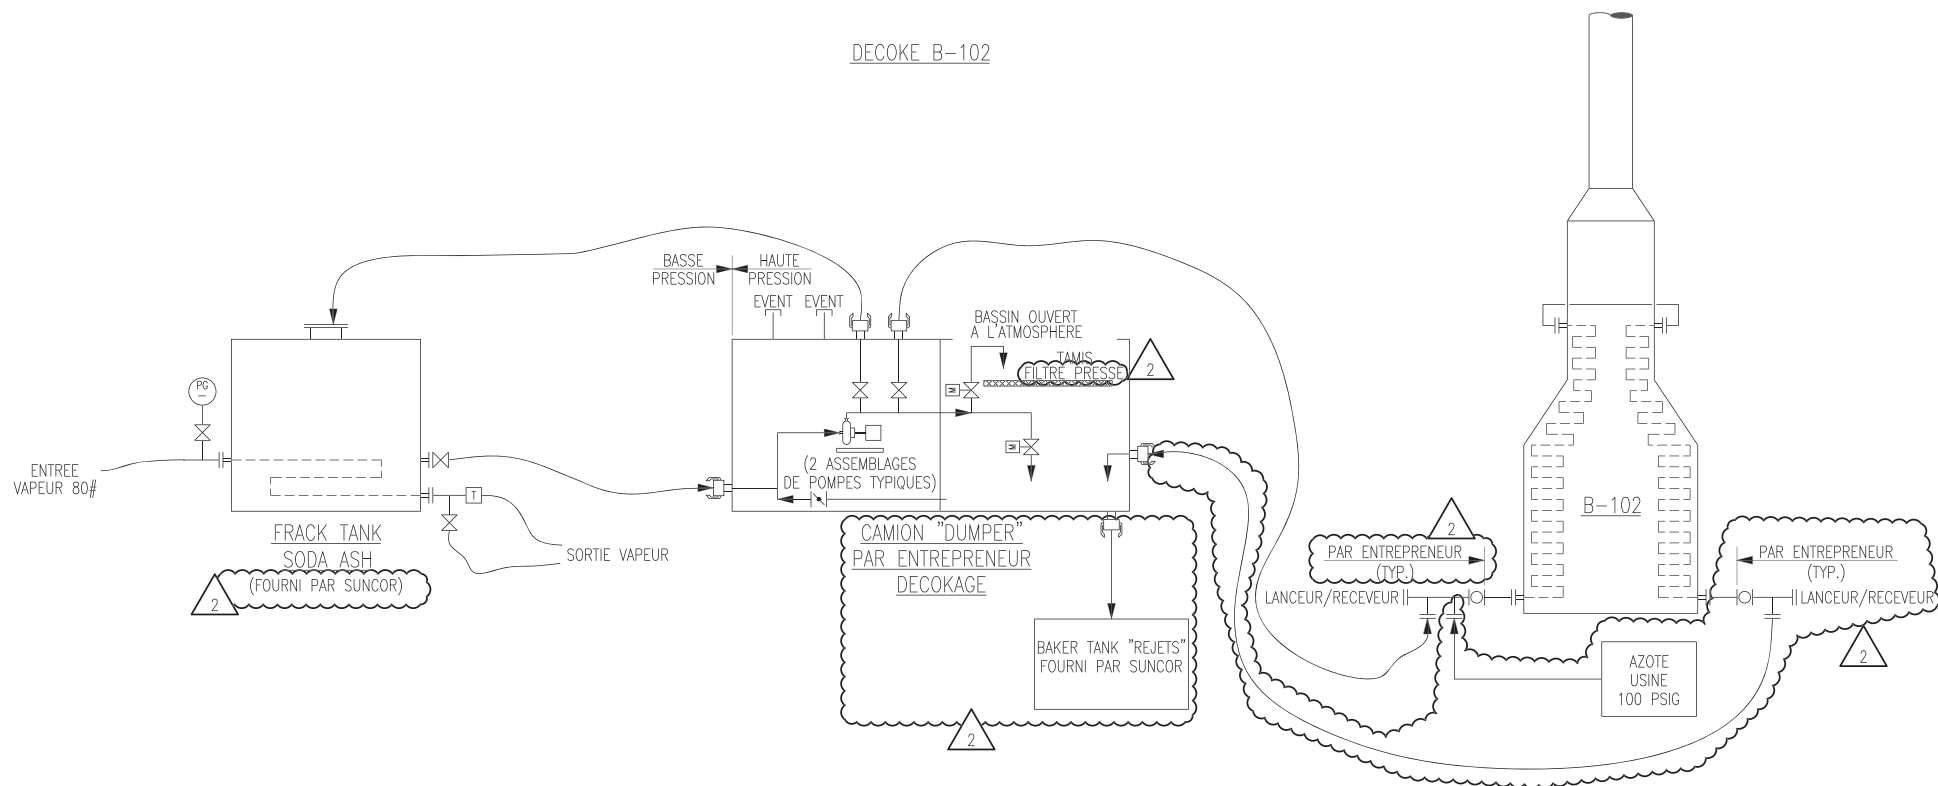

-	-
No. DESSIN	DESCRIPTION
DESSINS DE REFERENCE	
 UNITE DE BRUT #1 CROQUIS POUR LE DECOKE DU B-102 SECTION RADIANTE	CONCEPTEUR M. LECLAIR
	DESSINATEUR M. LECLAIR
	VERIFICATEUR S. CHEVRIER
	SUPERVISEUR ING. S. CHEVRIER
	DATE 24 NOVEMBRE 2017
	ECHELLE N/A
CLASSE G	No. DE DESSIN 010-067B0001
	REV 2

No.	DATE	REVISION	PAR	VERIF	ING. PROJET No. Enregistrement	APPR
2	2020 24 FEV	DECOKAGE DU B-102 SECTION RADIANTE - REVISION GENERAL PLAN FINAL (ORD.60093258)	A.R.	CFL	K. HAMDAN	
1	2017 24 NOV	CROQUIS POUR LE DECOKAGE DU B-102 PLAN FINAL (ORD.55030671)	M.L.		S. CHEVRIER	S.C.



LINE NUMBER

B0102

MK3 entrance
convection WEST
4"-300#

MK1 exit
convection EAST
4"-300#

MK5- 4"-300#

MK4- 4"-300#

Installation of decoke spool
B-102 MK-6 (Remove
sections mentioned at
M01B042A & B

B-102

VUE DU SUD
VERS NORD


entrance radiant
WEST 8"-300#

Installation launchers/receivers 8"-300#
(Remove sections B34-1 to 5 and 11 to 15 under nitrogen
purge)

exit radiant EAST
8"-300#

04/05-TP
03/03-TP


Rev. 11/99-IP

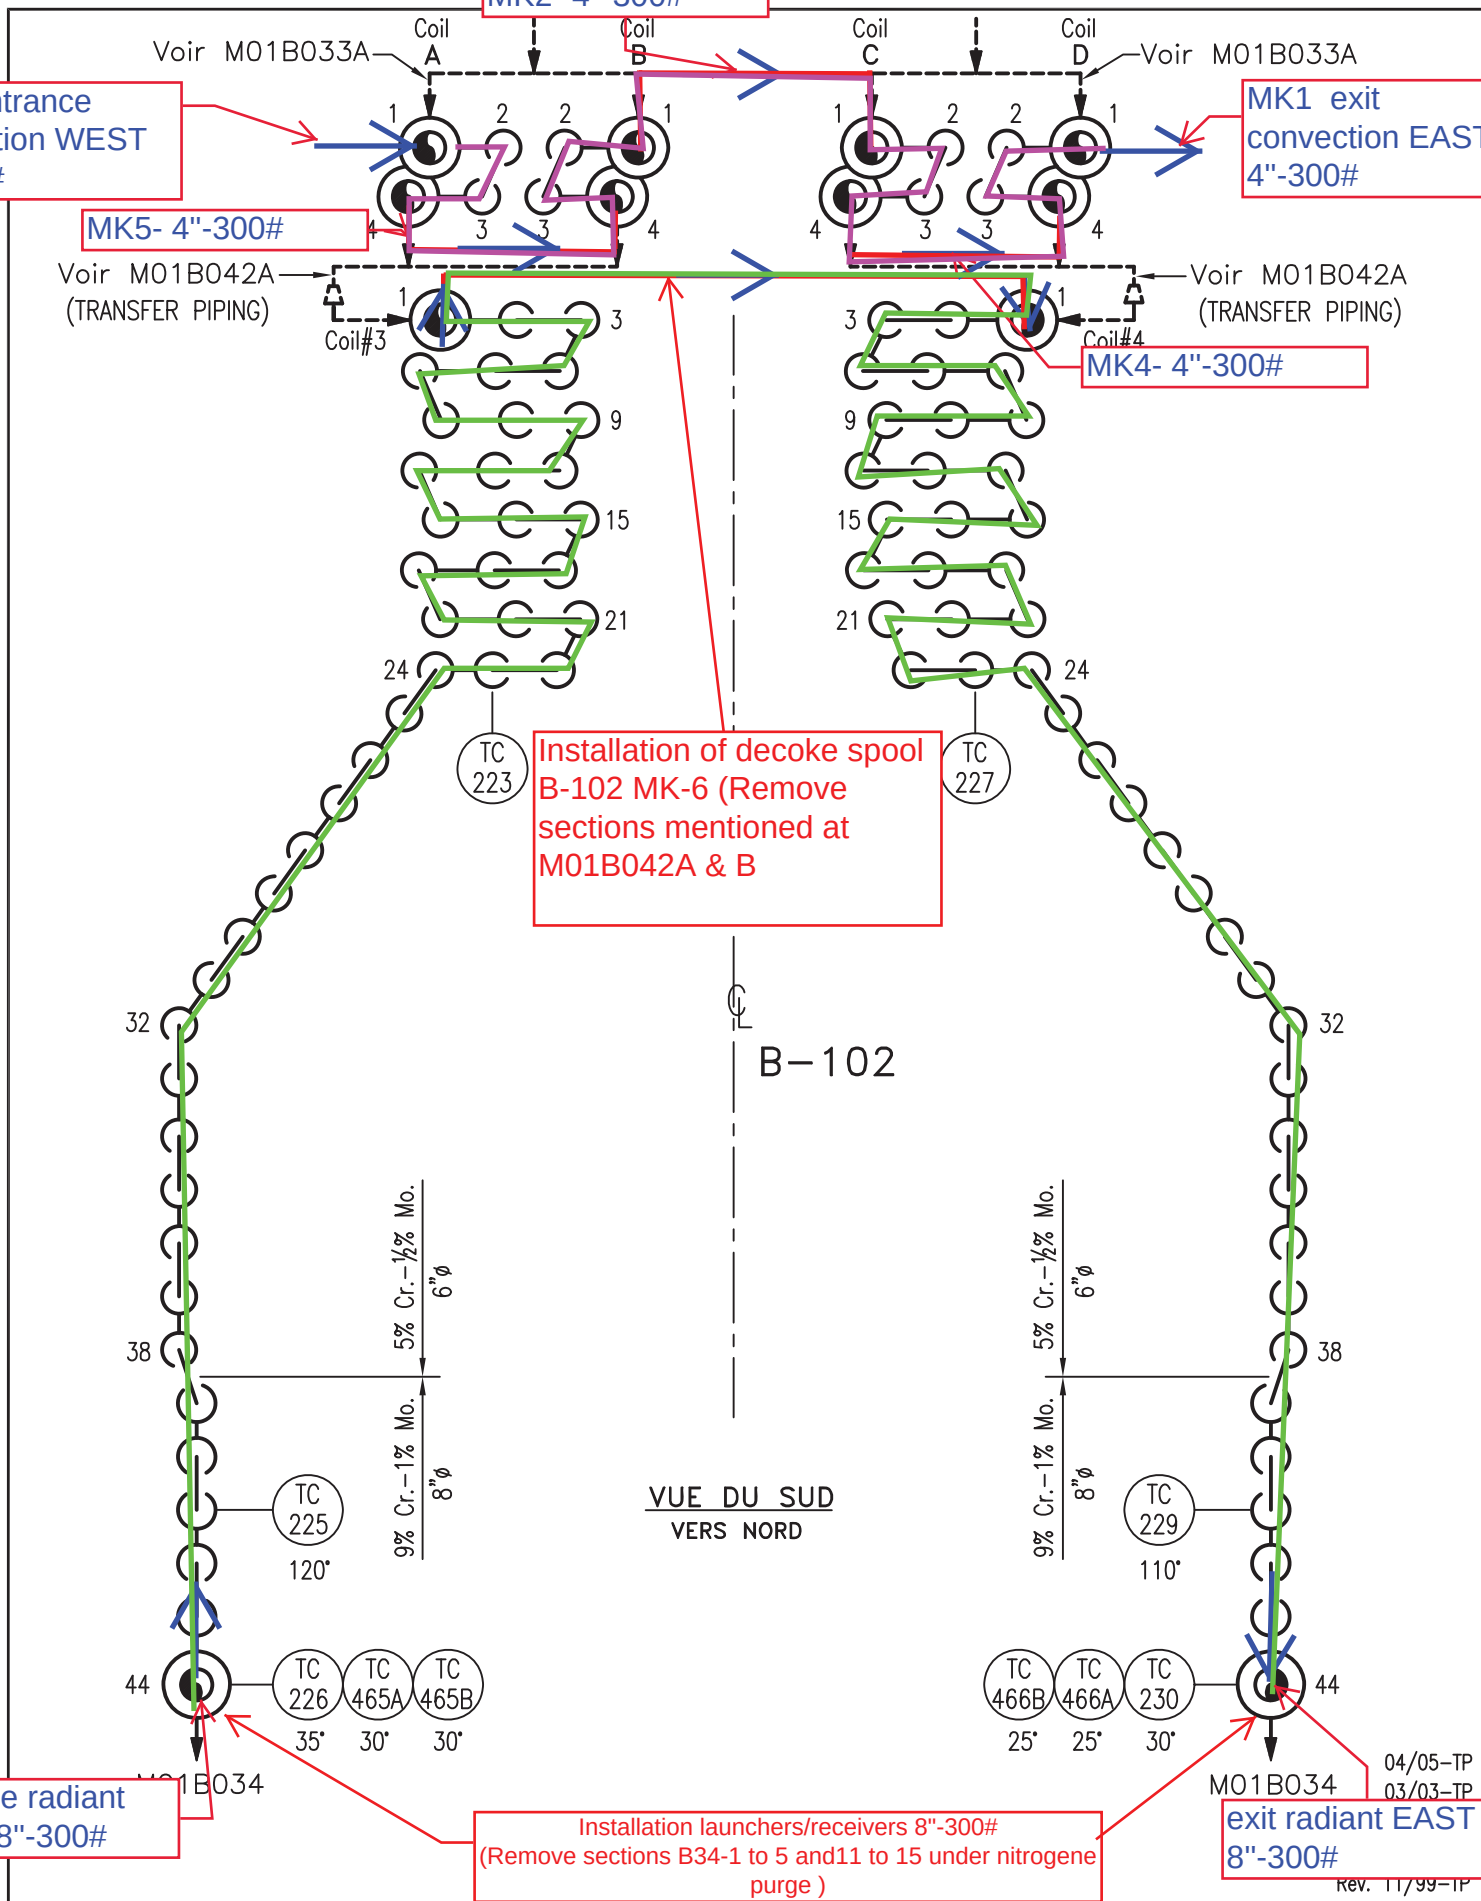

#01 BRUT

PRÉDISTILLATION DU C-152 AU B-102

1650

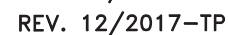

REFINERY

MONTREAL

UNIT


#01 BRUT

LINE DESCRIPTION

BRUT DE B-102 VERS E-101

(O-1464-12"-UD 317L)

(O-1465-12"-UD 317L)

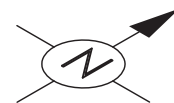

1670

plaque


Voir M010B035

démanteler spool
11 a 15 sous purge
azote

plaque

démanteler spool 1
a 5 sous purge
azote

Entrance and exit for decoking
radiant B-102 (8" X #300)
qty 02

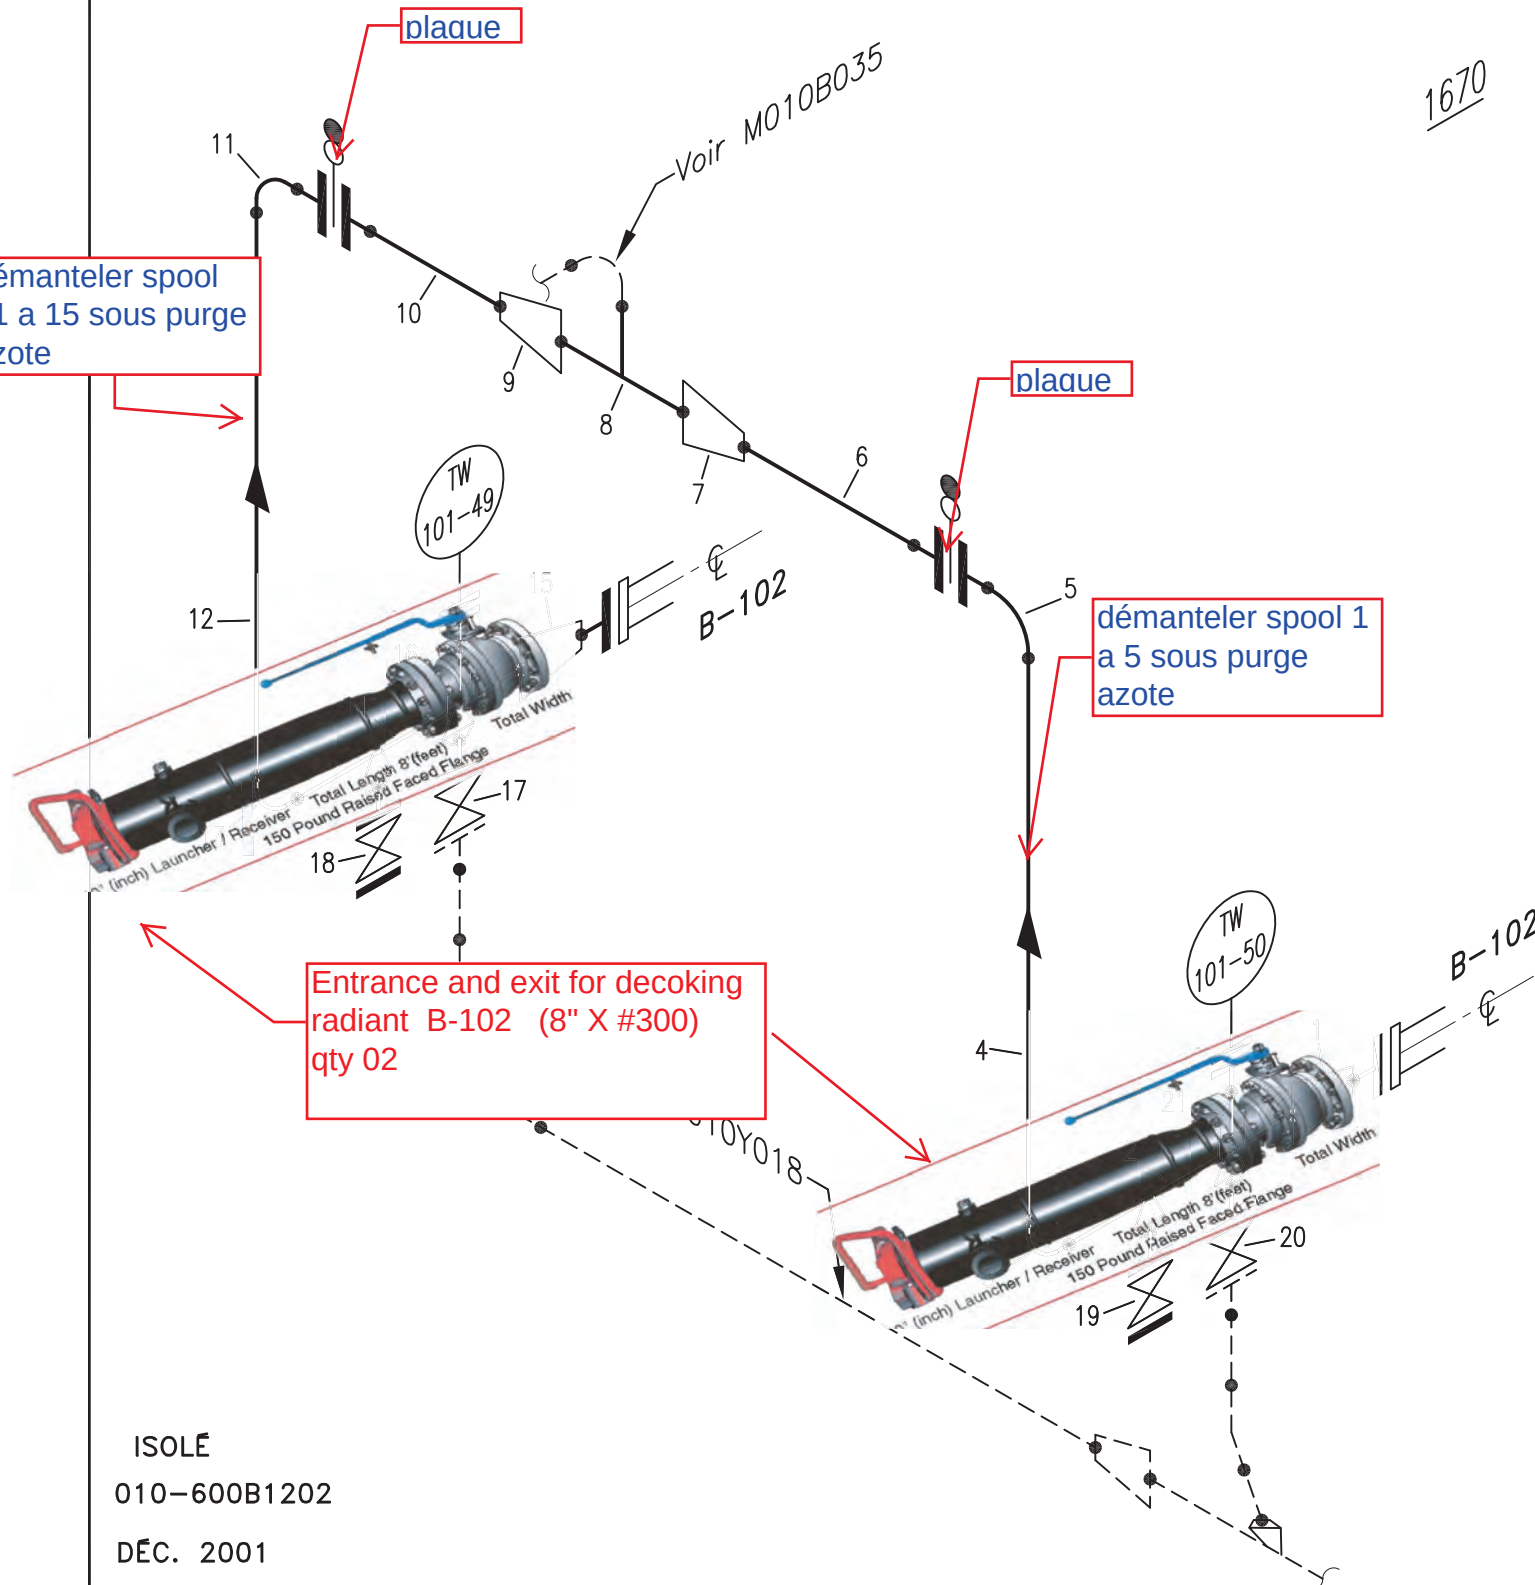


ISOLÉ

010-600B1202

DÉC. 2001

T.PHAM

REV. 0

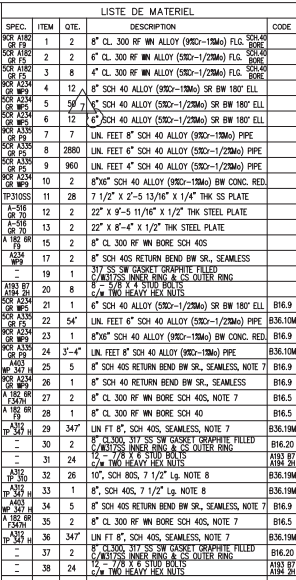[illegible]

2. **CONTRAT DE QUALITE DES SERVICES**
 2.1. **SECONDE PARTIE SELON LE STANDARD CUS-213** POUR LE 50%, 90% ET 347H
 2.2. **55247H**
 2.3. **EFFICACITE DES TESTS DE FERRITE SUR LES JOINTS DE SoudURE de**
 2.4. **LA PARTIE EN TRAITEMENT THERMIQUE DE STABILISATION A 1650F° SELON**
 2.5. **LA SoudURE (100% PAR SoudUREUR) SELON API 580 71.2.4 (AUTENTIQUE)**
 2.6. **550/0/0/0**
 2.7. **100% METEOROLOGIE DES SOURCES D'ONDES DIFFERENTIELLES**
 2.8. **100% METEOROLOGIE DES SOURCES D'ONDES DIFFERENTIELLES**
 2.9. **550/0/0/0**
 2.10. **550/0/0/0**
 2.11. **550/0/0/0**
 3.1. **SECONDE PARTIE SELON LE STANDARD CUS-213** POUR LE 50%, 90% ET 347H
 3.2. **55247H**
 3.3. **EFFICACITE DES TESTS DE FERRITE SUR LES JOINTS DE SoudURE de**
 3.4. **LA PARTIE EN TRAITEMENT THERMIQUE DE STABILISATION A 1650F° SELON**
 3.5. **LA SoudURE (100% PAR SoudUREUR) SELON API 580 71.2.4 (AUTENTIQUE)**
 3.6. **550/0/0/0**
 3.7. **100% METEOROLOGIE DES SOURCES D'ONDES DIFFERENTIELLES**
 3.8. **100% METEOROLOGIE DES SOURCES D'ONDES DIFFERENTIELLES**
 3.9. **550/0/0/0**
 3.10. **550/0/0/0**
 3.11. **550/0/0/0**
 3.57.


010-80800027	8-102, EMPLACEMENT DES THERMOCOUPLES DE PEAU. DESSIN LOCALISATION
01021900001	ELEVATION, COUPE ET DETAILS
57133-1	ASSEMBLY AND CONTROL DWG. - CRUDE OIL HEATER
NO.	DESSIN DE REFERENCE



UNITE DE BRUT #1
B-102
PORTION DES TUBES REMPLACEES
ELEVATION DE COTE OUEST/EST


DESSEIN/	M.AUGUSTYNIAK	DATE/	SEPT.20/2001	FILIERE/	INGENIERIE
CONCEPT/	L.R.PREVILLE	VERGEE/	G.C.	FICHIER/	AUTOCAD
EDIELLE AUTOCAD/	NOTE 10	CLASSE/	NO. DU DESSIN/	REV/	
EDIELLE/	3/8"=1'-0"	B	010-219D0002	7	

CODE DE SERVICE	SERVICE OU SPECIFICATION	CODE DE REPARATION	NO. D'ENREGISTREMENT CANADIEN (N.E.C.)	NO. SERIE	PRESSION DE CONCEPTION	PRESSION D'ESSAI	TEMPERATURE MINIMUM DE CONCEPTION DU MATL (MILM)	TEMPERATURE DE CONCEPTION	SURPAISSEUR DE CONCEPTION	ESSAI NON DESTRUCTIF	TRAIT. THERMIQUE	SOUPAPE DE PROTECTION	REGIE PAR LA RBQ	EPAISS. D'O.S. - MATL	TEST D'IMPACT
B-102	BRUT	B31.3-2016 NORMAL FLUID SERVICE (NOTE 1)	QF1-28	-	VOIR CONDITIONS	1080 PSIG (NOTE 1)	-20 °F	VOIR CONDITIONS	0.0625"	NOTE 2 & 6	NOTES 2,6 & 7	RV-B-102B/C	OUI	N/A - N/A	NON

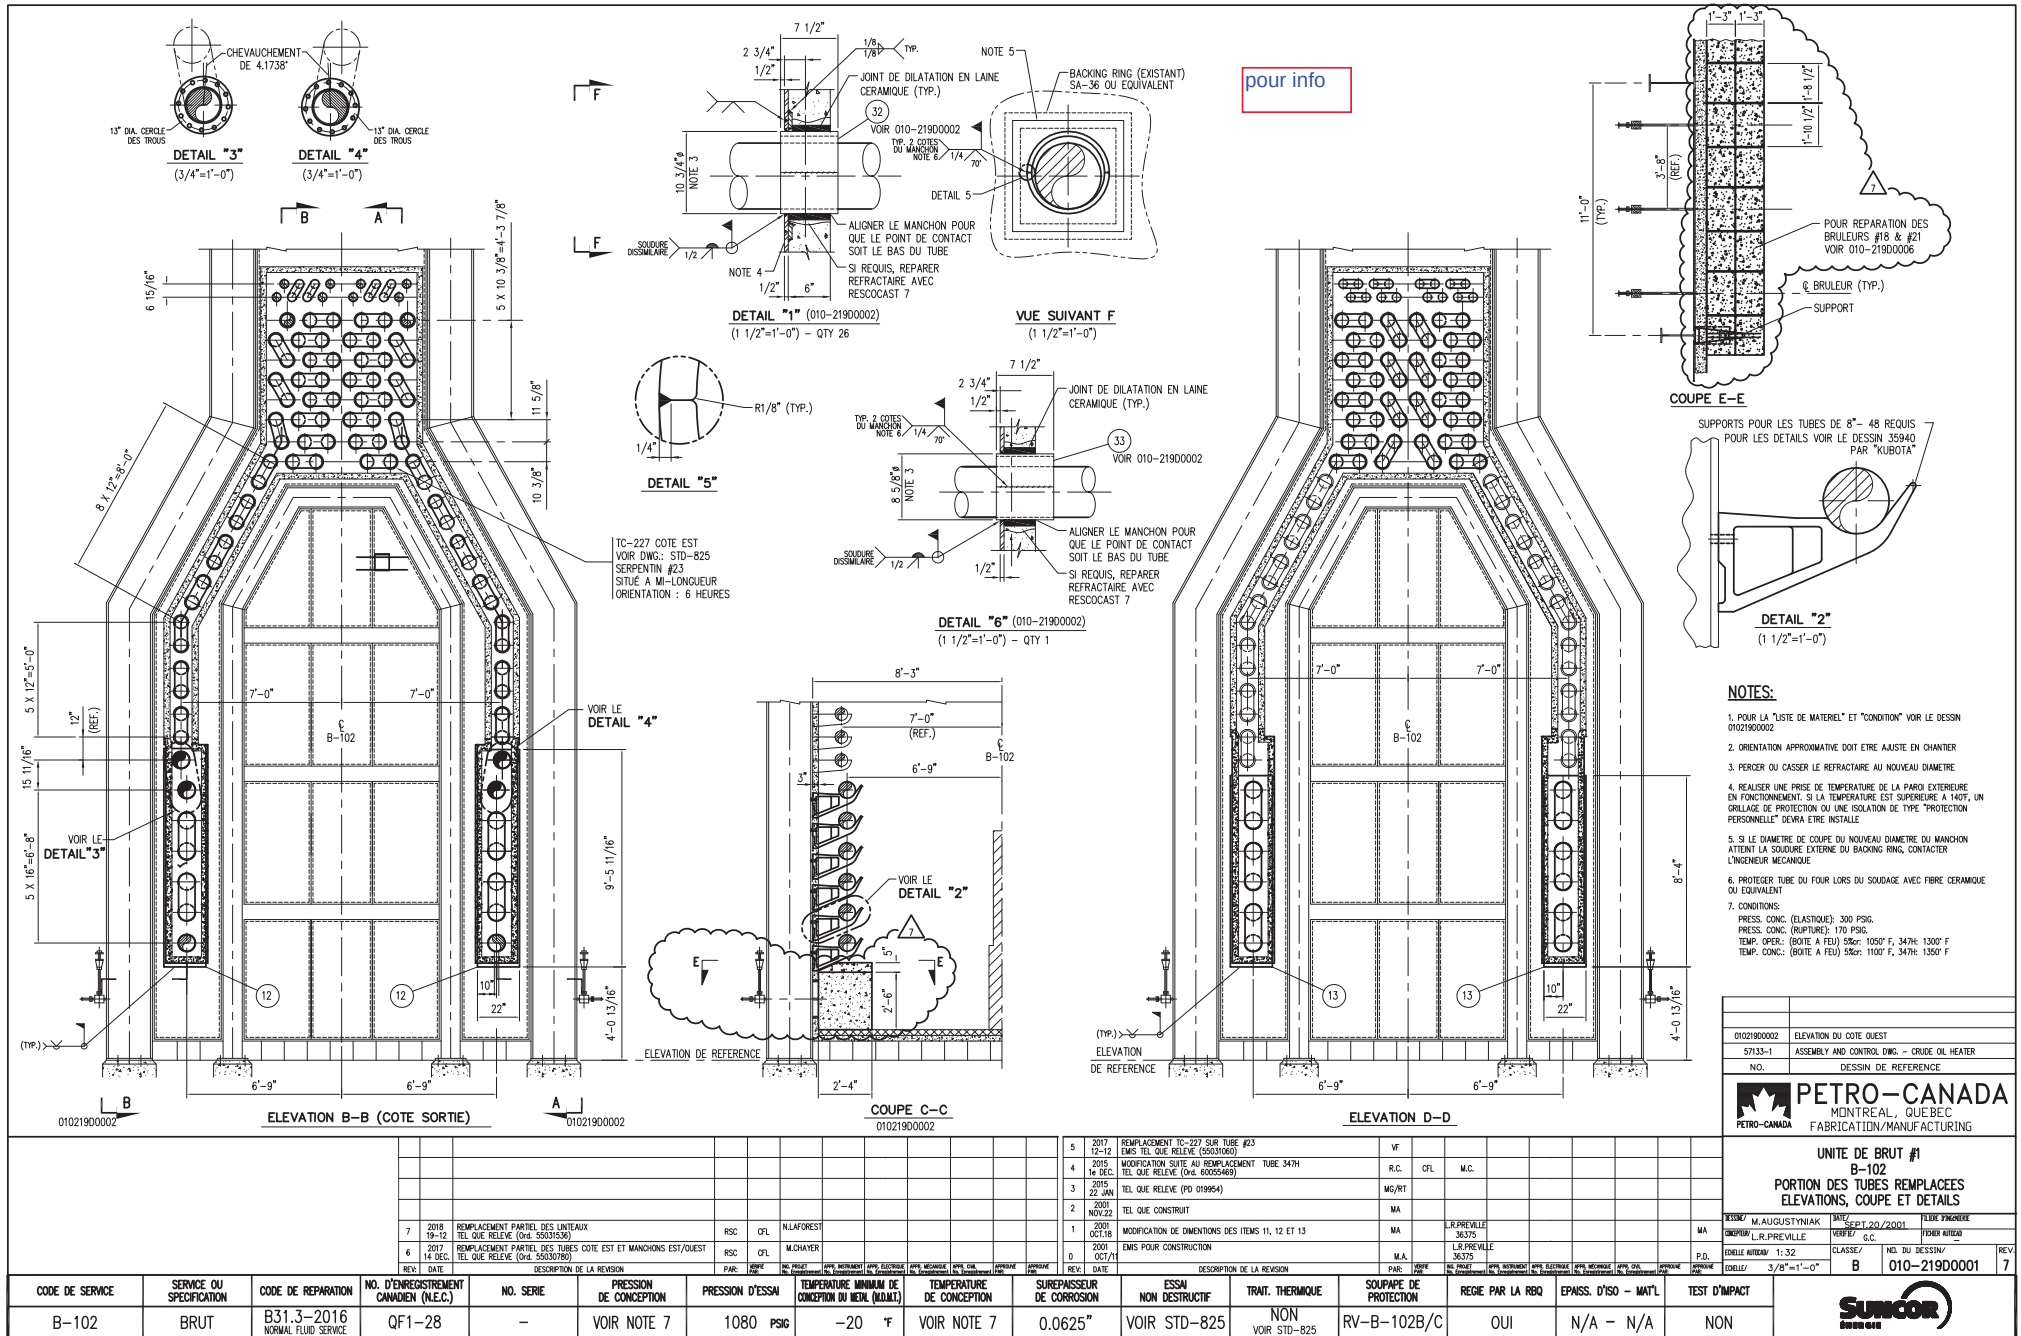



pour info

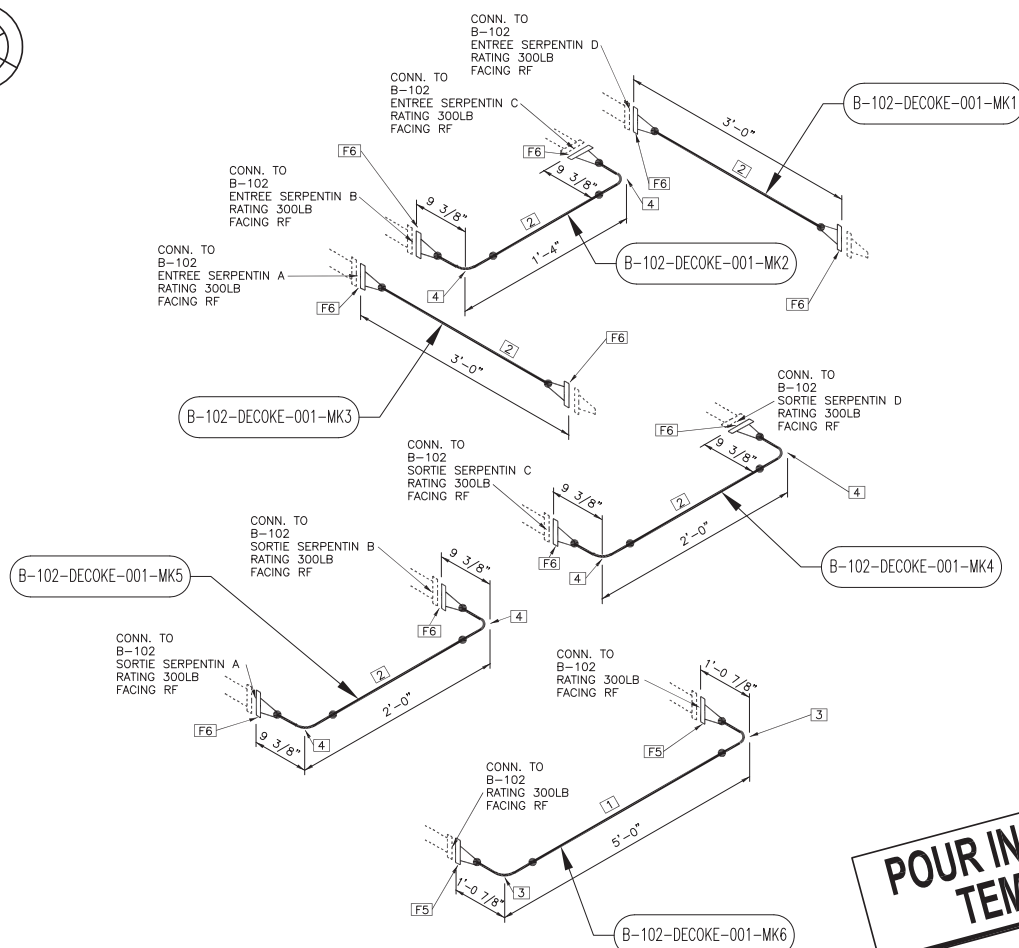

NOTES:

1. VERIFIER TOUTE LES DIMENSIONS AU CHANTIER AVANT LA FABRICATION.
2. REGIE RBQ: NON
3. INSTALLER UNE PLAQUE D'IDENTIFICATION EN SS SUR CHAQUE SPOOL ET Y INSCRIRE:
 - NO ISOMETRIQUE: 010-600B1474
 - NO SPOOL: B-102-DECOKE-001-MK1 ET/OU B-102-DECOKE-001-MK2 ET/OU B-102-DECOKE-001-MK3 ET/OU B-102-DECOKE-001-MK4 ET/OU B-102-DECOKE-001-MK5 ET/OU B-102-DECOKE-001-MK6 ET/OU
 - SPEC: UD1
 - ANNEE DE FABRICATION
4. PEINDRE LE SPOOL TEMPORAIRE DE COULEUR: ORANGE FLUORESCENT.

P&ID	010-062D0006
AIRE D'UNITE	010A01
DESSINS / REFERENCES	NO. DESSINS / NO. REFERENCES
SUNCOR CLASSE INSPECTION / END	S III
VE 100%	RT 10%
CHANFREIN	

LISTE DE MATERIEL

No	QTE	DIA	DESCRIPTION	NORME / CODE
1	3'6"	6	Pipe, A106-B, SMLS, Sch Std, BBE	ASME B36.10M
2	7'3"	4	Pipe, A106-B, SMLS, Sch Std, BBE	ASME B36.10M
3	2	6	EI - 90, LR, BW, A234-WPB, Sch Std	ASME B16.9
4	6	4	EI - 90, LR, BW, A234-WPB, Sch Std	ASME B16.9
5	2	6	WN Flg, A105N, CL300, Sch Std, RF	ASME B16.5
6	10	4	WN Flg, A105N, CL300, Sch Std, RF	ASME B16.5

2	2018 12 DEC	SPOOLS TEMPORAIRES DECOCKAGE FOUR B-102 EMIS POUR PLAN FINAL (0.60086947)	MeG	CFL	K.HAMDAN	
1	2018 05 AVRIL	SPOOL TEMPORAIRE DECOCKAGE FOUR B-102 EMIS POUR PLAN FINAL (Ord.55031532)	RSC MeG	CFL		
No.	DATE	REVISION	PAR	VERIF	ING. PROJET No. Enregistrement	APPR

SUNCOR ENERGIE		CONCEPTEUR		R.SCHULER	
		DESSINATEUR		R.SCHULER	
		VERIFICATEUR		C.LY	
		SUPERVISEUR ING.		S.ARCAND	
		DATE		26/03/2018	
010 BRUT #1 SPOOLS TEMPORAIRES POUR DECOCKAGE FOUR B-102 B-102-DECOKE-001-MK1 @ MK6		ECHELLE		AUCUNE	
		CLASSE	No. DE DESSIN		REV
		M	010-600B1474		2

REFINERY

MONTREAL

UNIT


#01 BRUT

LINE DESCRIPTION


FOND DE PRE-DÉTENTE DE LA SECTION CONVECTION A LA SECTION RADIANT DU B-102

(O-1467-6"/4"-UD10)

pour info

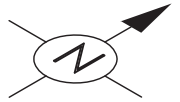

1650

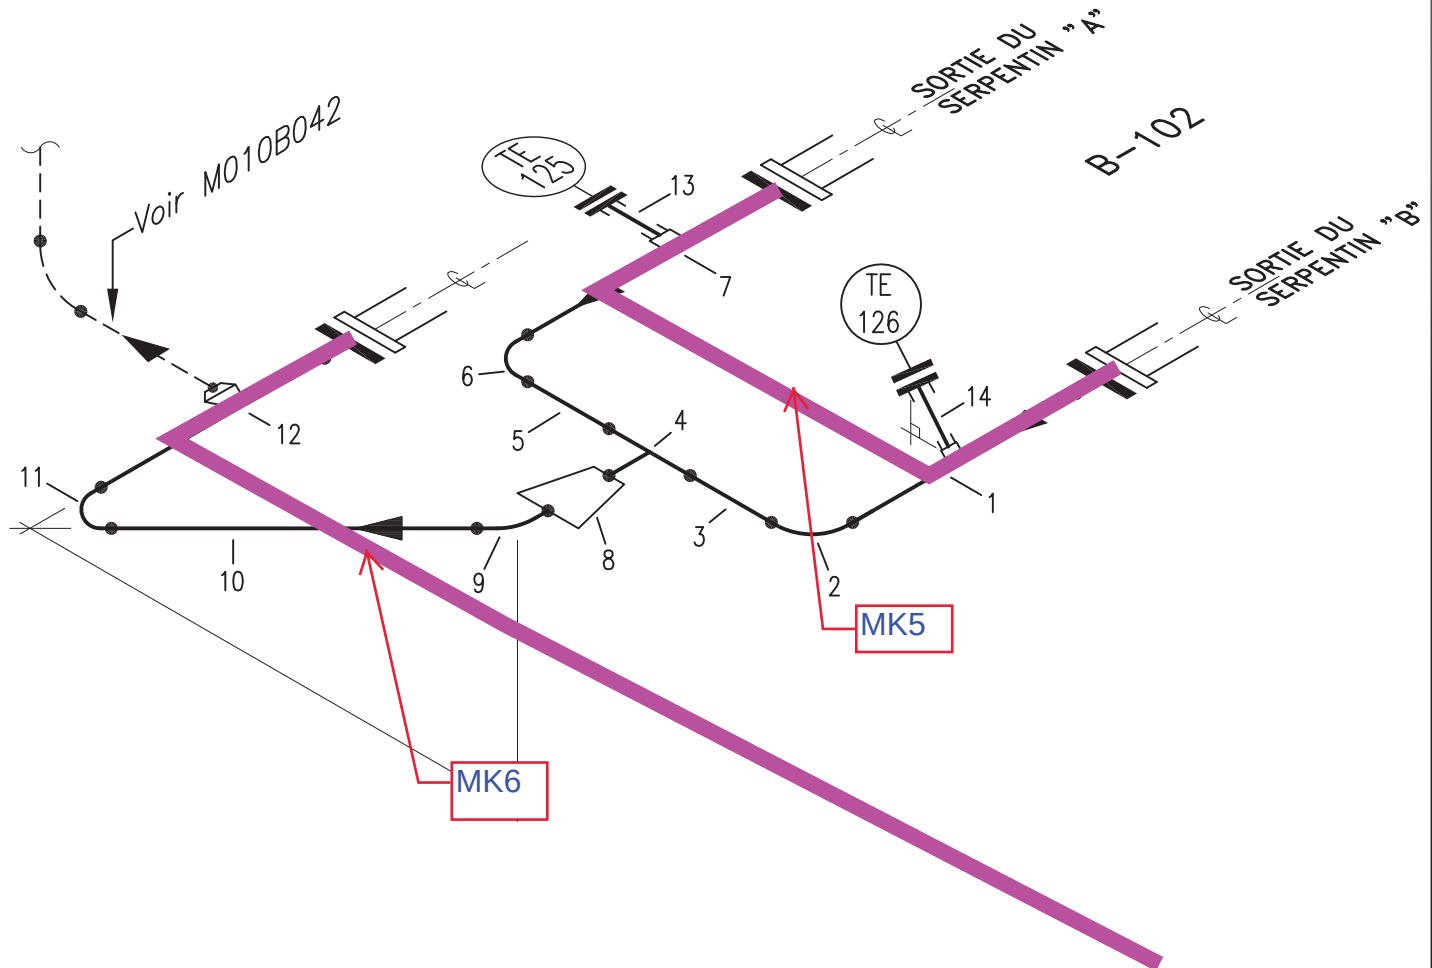

PART. ISOLÉ
010-600B0944
SEPT. 1998

T.PHAM

REV. 01/2002-TP

SAP# 100006198

LINE NUMBER

M010B042B

REFINERY

MONTREAL

UNIT


#01 BRUT

LINE DESCRIPTION


FOND DE PRE-DÉTENTE DE LA SECTION CONVECTION A LA SECTION RADIANT DU B-102

(O-1468-6"/4"-UD10)

pour info

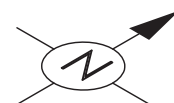

1660

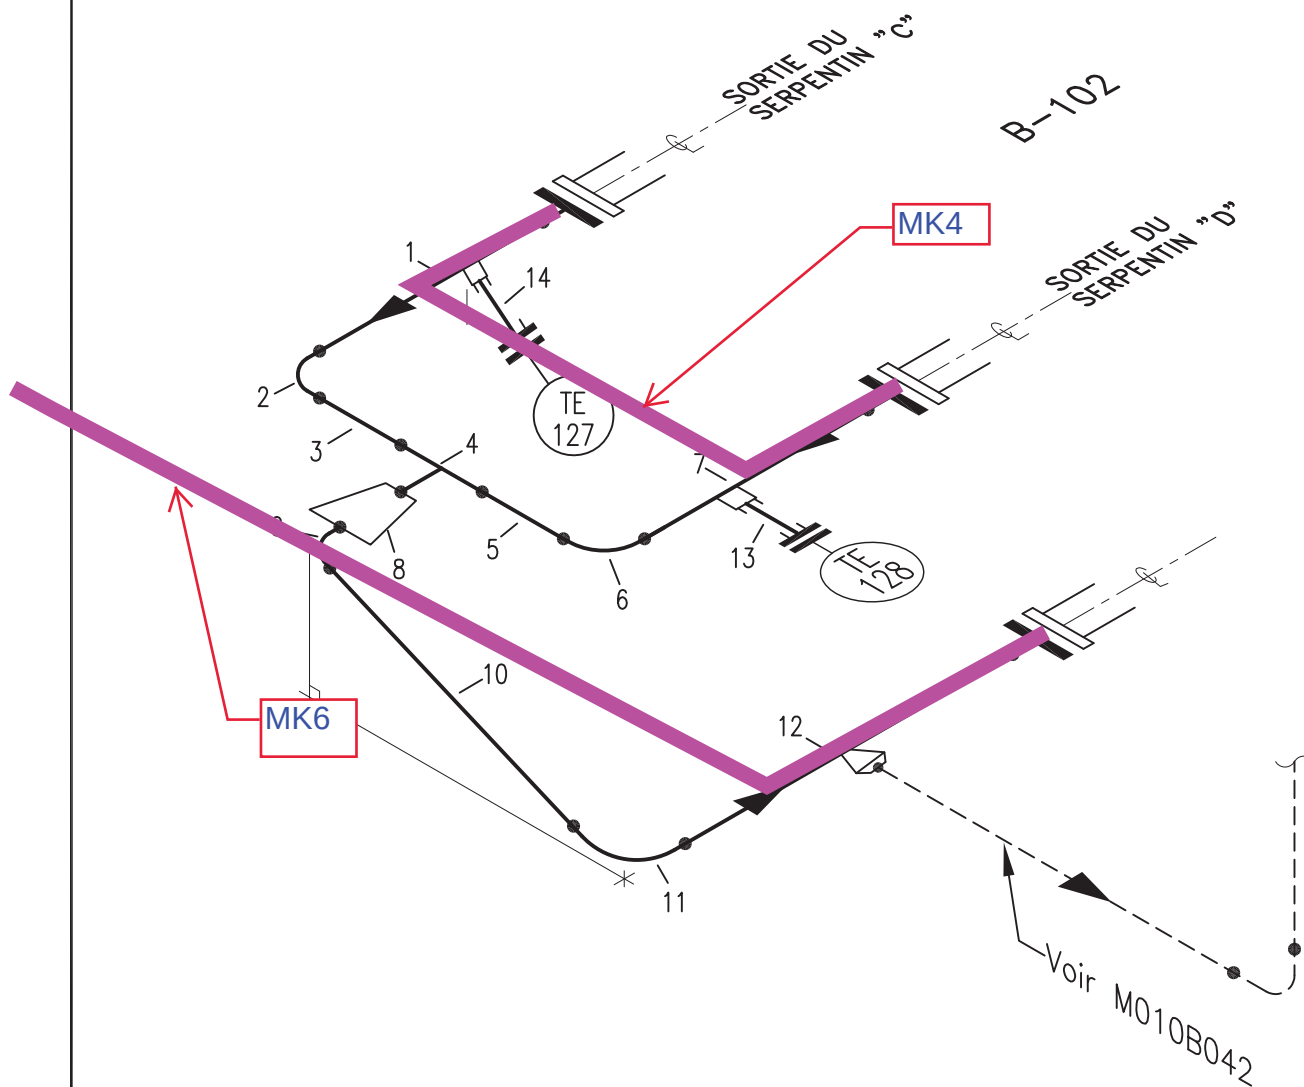

PART. ISOLÉ

010-600B0945

SEPT. 1998

T.PHAM

09/2014-NL
REV. 01/2002-TP