


F-901 FIRED HEATER DECOKING

SINGLE TRIMAX / TRIPLE MODE OPERATION

EXXONMOBIL BAYTOWN — PS8 (KHF)

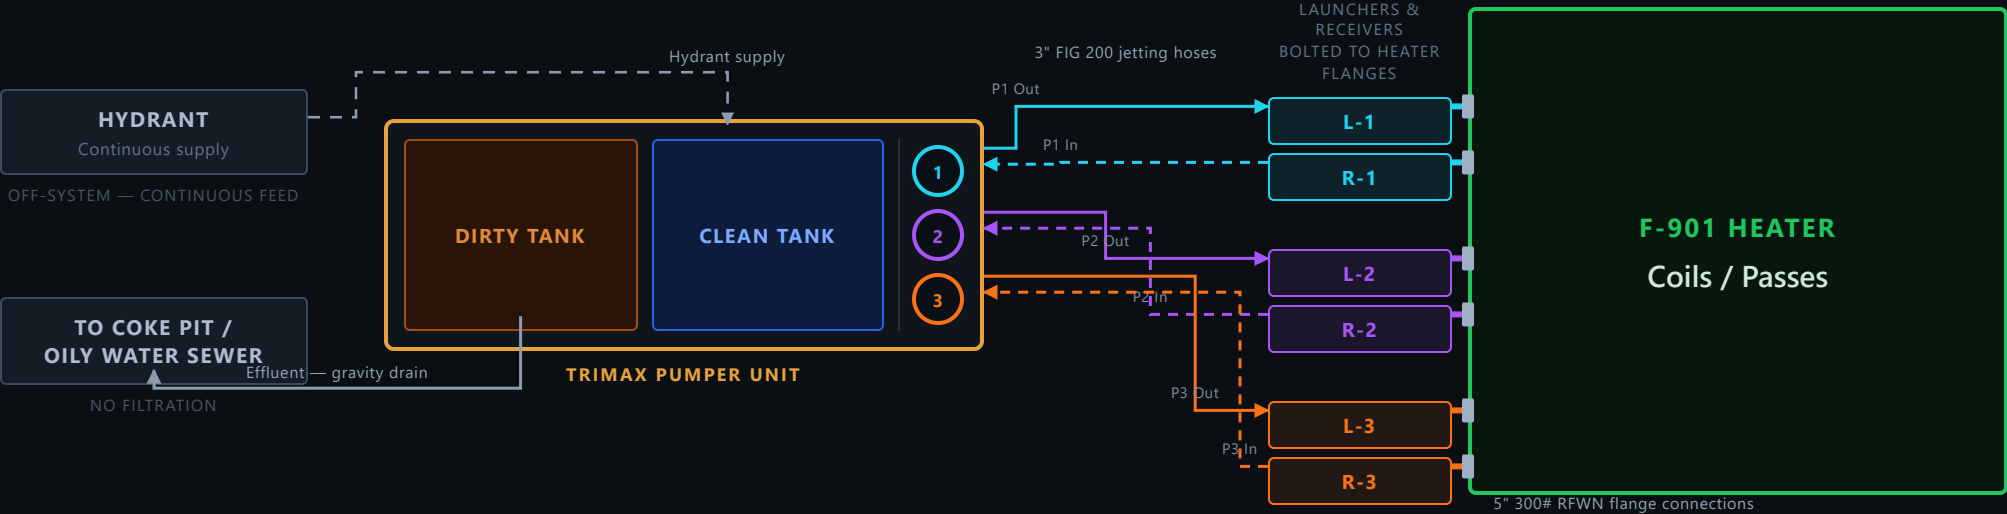

CIRCUIT ASSIGNMENTS

Pass 1 — Process Coils (Convection + Radiant)

Two coils looped via JS-1 | 3,168 ft | 5.043" ID

Pass 2 — Treat Gas

Single Pass | 896 ft | 5.043" ID

Pass 3 — Superheat Steam

Single Pass | 136 ft | 5.047" ID

HEATER ARCHITECTURE

Connections: 5" 300# RFWN

Launchers/Receivers: 6 Total (Grade Level)

Adapters: 5" x 6" 300# RFWN

Pig Sizing Increment: 1/8" per pass

Max Pig OD: 5.25" (rule cap: 5.043" ID + 0.250", rounded down)

EQUIPMENT SCOPE

TriMax: 1 Unit (Triple Mode)

Water Source: Hydrant — continuous supply

Filtration: None — declined

Effluent: Coke pit / oily water sewer

Inspection: Steady-Flux Smart Pigging